



11 |0 |0.5m |1.25m |2.5m|

## SEZIONI - SCALA 1:10

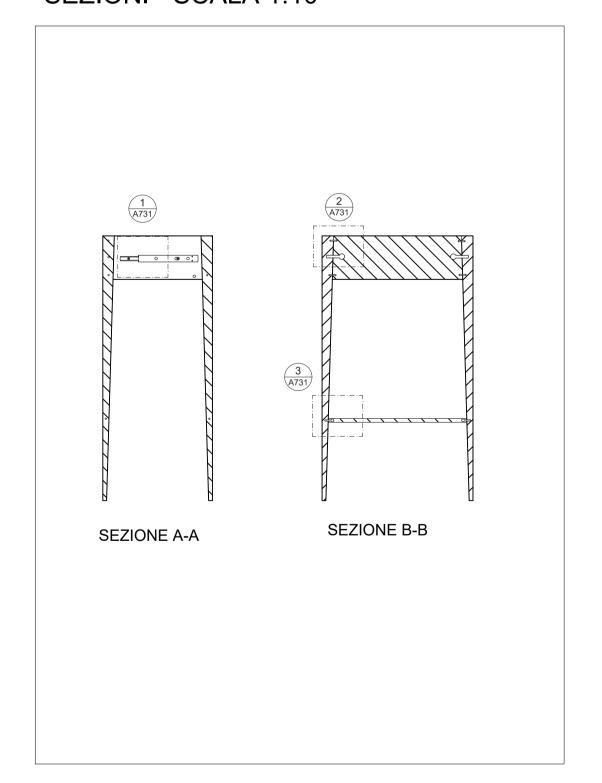

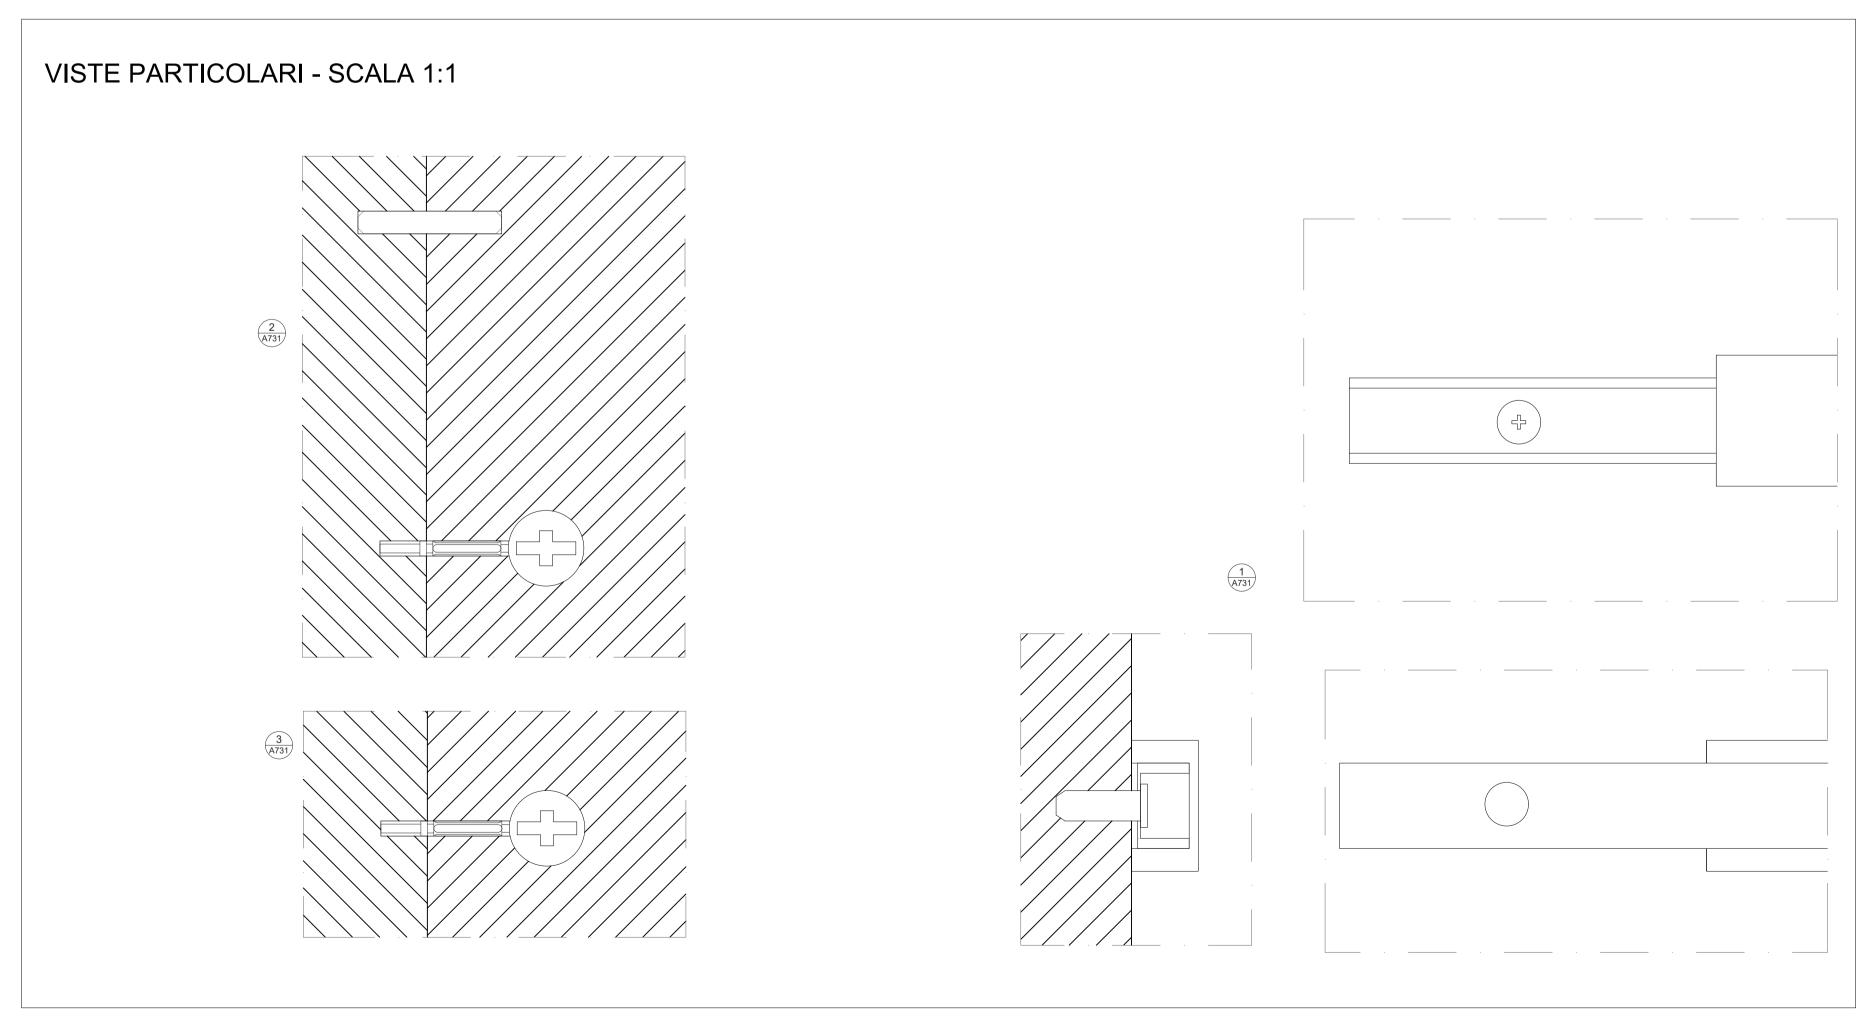

POLITECNICO DI MILANO
SCUOLA DEL DESIGN
C.L. DESIGN DEGLI INTERNI
PROGETTO:

QM-D\_4

CORSO:
STRUMENTI E METODI
DEL PROGETTO

DOCENTE:

MARCO FERRARA
STUDENTI:

Francesca Martelli

OGGETTO:

COMODINO HEMNES\_901-212-34

NOME FILE:

HEMNES\_901-212-34.DWG

VERS DA

2017/07/17
2017/06/16
2017/05/23

A 2017/05/15

TAVOLA NO.: 003 DI 004

A731

DATA: 2017/07/17 SCALA: VARIE REV: A FORMATO: A1